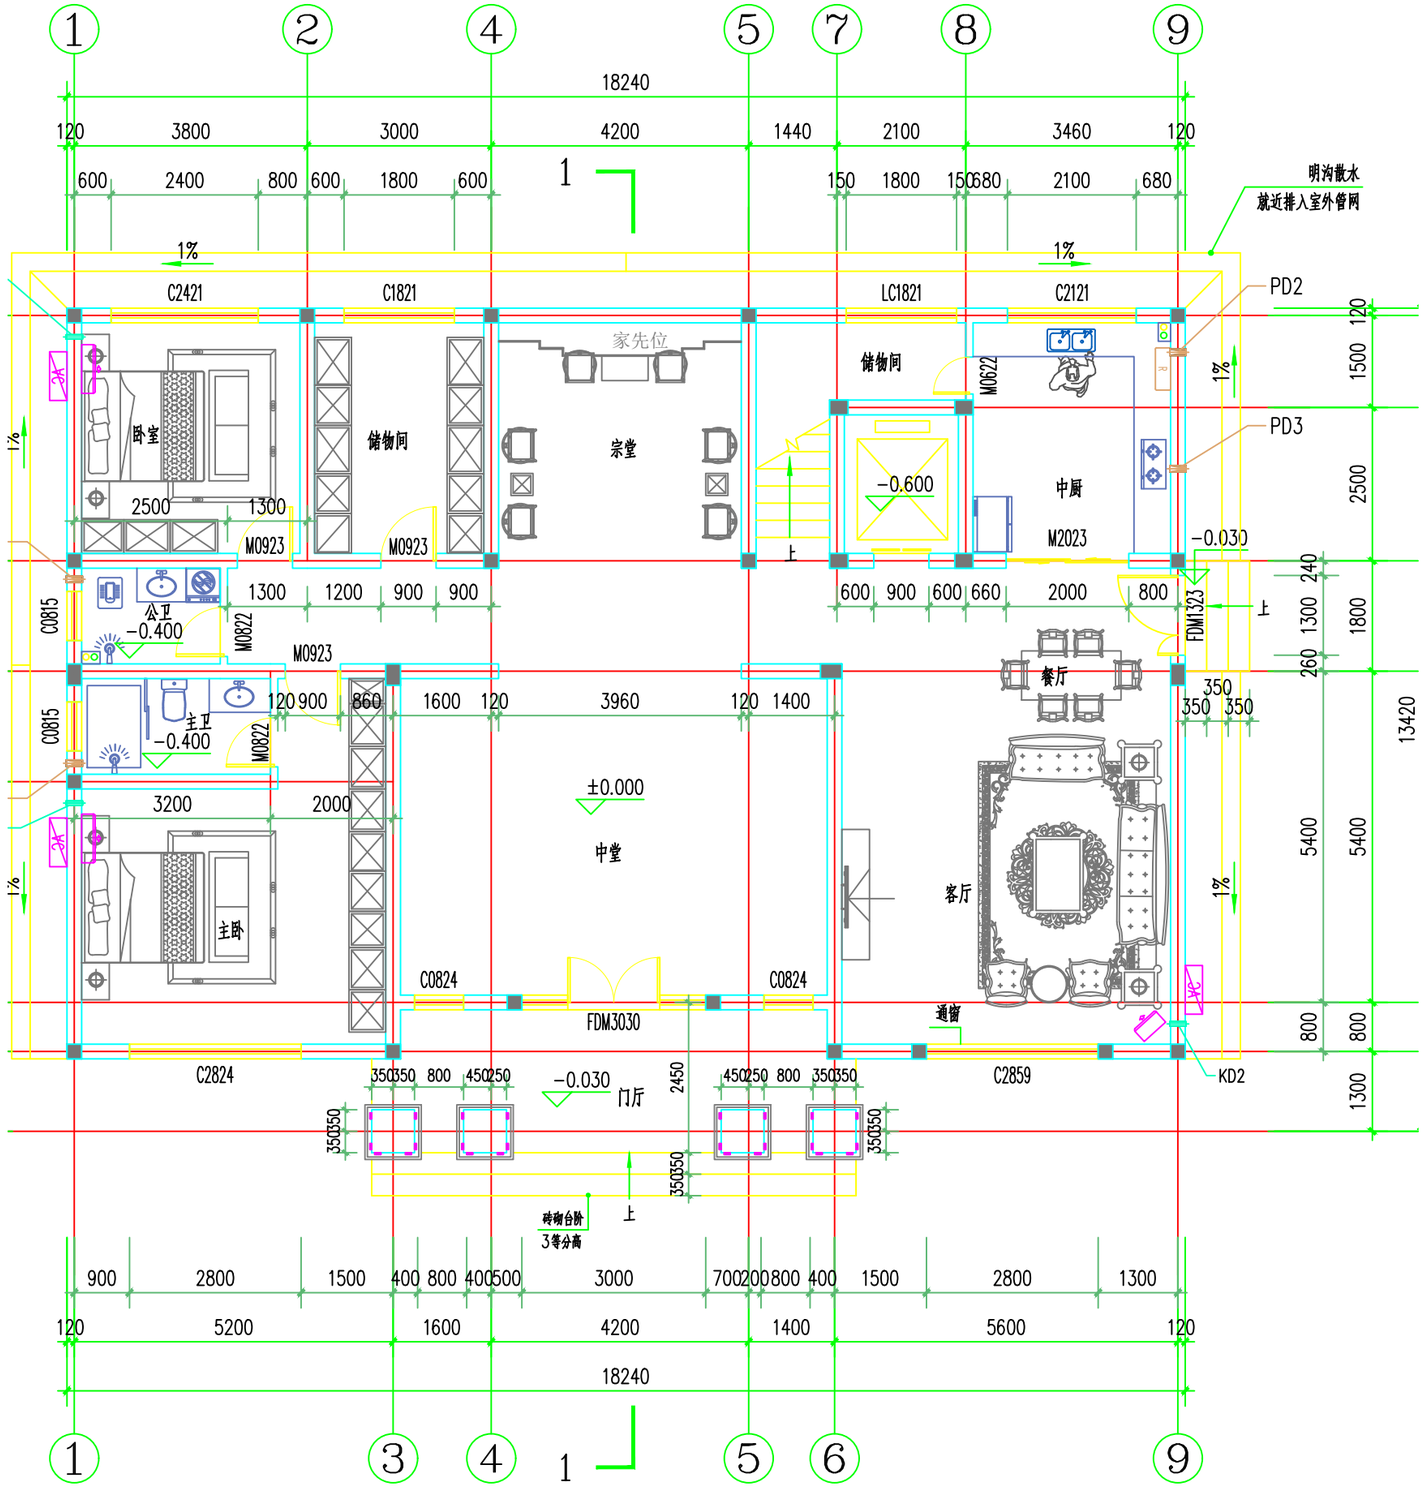
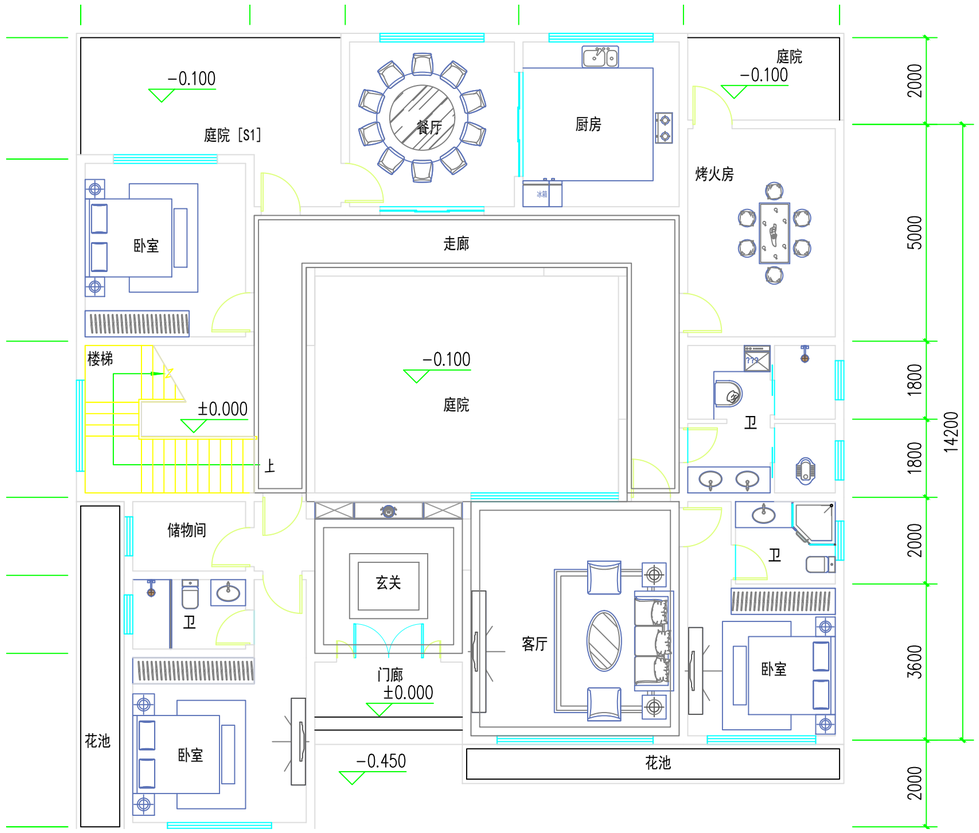

1
2
4
5
7
8
9
18240
120
3800
3000
4200
1440
2100
3460
120
600
2400
800
600
1800
600
150
1800
150
680
2100
680
明沟散水
就近排入室外管网
1%
C2421
C1821
LC1821
C2121
PD2
PD3
卧室
储物间
家先位
宗堂
储物间
M0622
中厨
-0.600
M2023
-0.030
2500
1300
M0923
M0923
1300
1200
900
900
600
900
600
660
2000
800
FDM1323
C0815
公卫
-0.400
M0822
M0923
餐厅
C0815
主卫
-0.400
M0822
120
900
860
1600
120
3960
120
1400
350
350
350
3200
2000
±0.000
中堂
主卧
客厅
C0824
C0824
FDM3030
通窗
C2824
350
350
800
450
250
-0.030
门厅
2450
450
250
800
350
350
C2859
KD2
350
350
350
350
砖砌台阶
3等分高
上
900
2800
1500
400
800
400
500
3000
700
200
800
400
1500
2800
1300
120
5200
1600
4200
1400
5600
120
18240
1
3
4
5
6
9
1500
2500
240
1300
260
1800
13420
5400
5400
800
800
1300

一层平面图 1:100


-0.100
庭院［S1］
餐厅
厨房
庭院
-0.100
烤火房
卧室
走廊
楼梯
-0.100
庭院
±0.000
上
卫
储物间
玄关
卫
客厅
卧室
卫
门廊
±0.000
花池
卧室
-0.450
花池
2000
5000
1800
1800
14200
2000
3600
2000