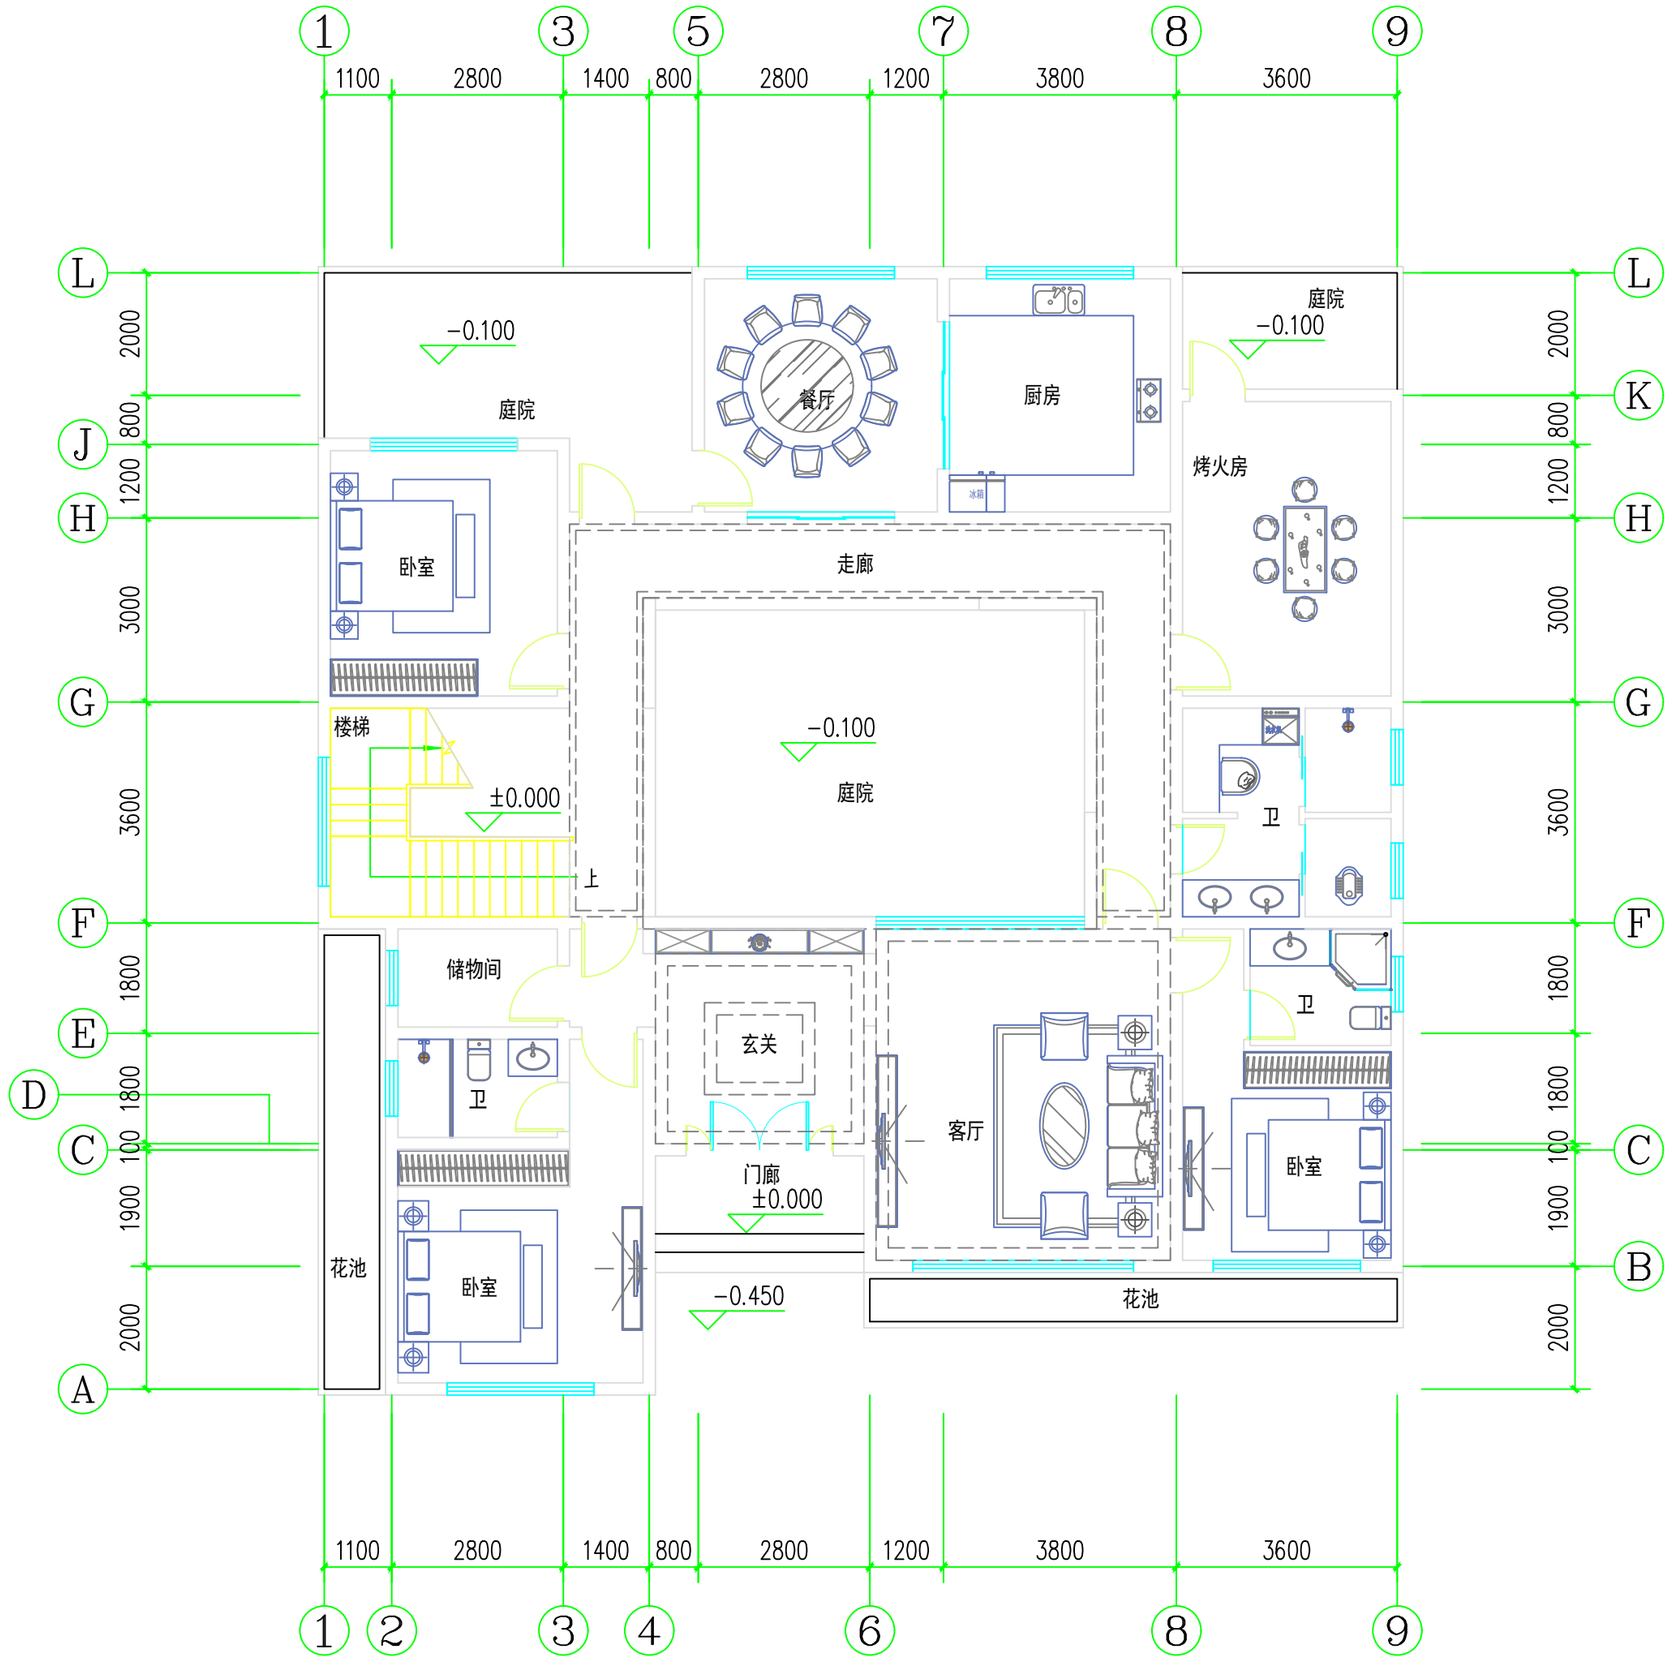

1
3
5
7
8
9
1100
2800
1400
800
2800
1200
3800
3600
L
J
H
G
F
E
D
C
A
K
B
2000
800
1200
3000
3600
1800
1800
100
1900
2000
−0.100
庭院
餐厅
厨房
冰箱
庭院
−0.100
烤火房
卧室
走廊
楼梯
±0.000
上
−0.100
庭院
卫
储物间
玄关
卫
卫
客厅
卧室
门廊
±0.000
花池
卧室
−0.450
花池
1100
2800
1400
800
2800
1200
3800
3600
1
2
3
4
6
8
9